


ALZADO

Escala 1:20


Viga superior

Escala 1:20

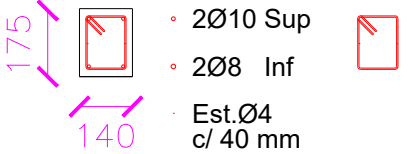


Columna

Escala 1:20

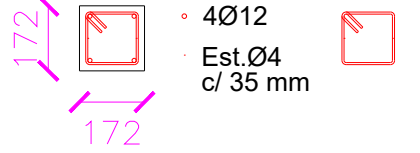



Viga inferior

Escala 1:20

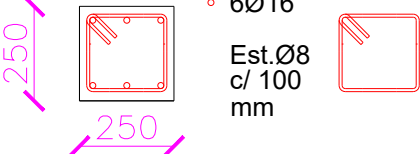


PLANTA

Escala 1:20

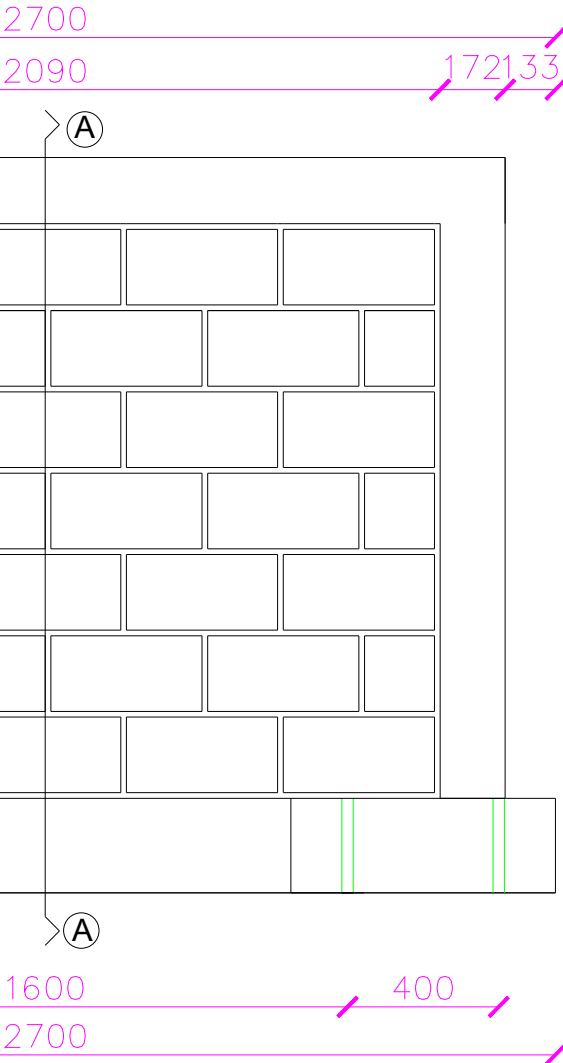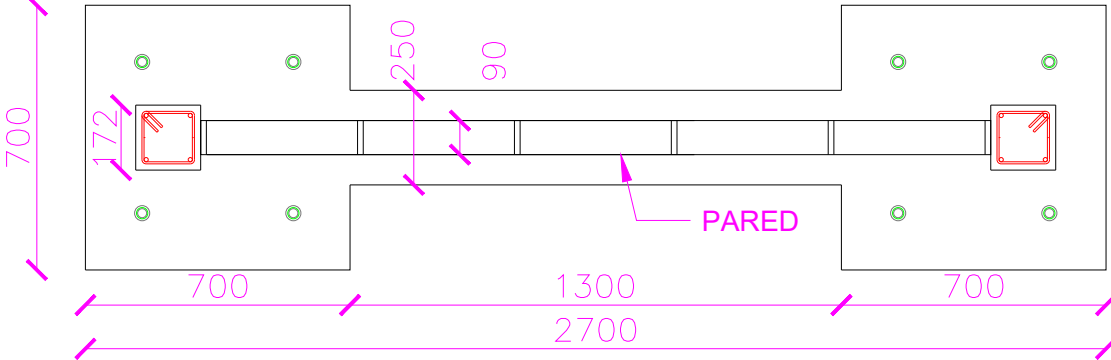


CORTE A - A

Escala 1:20

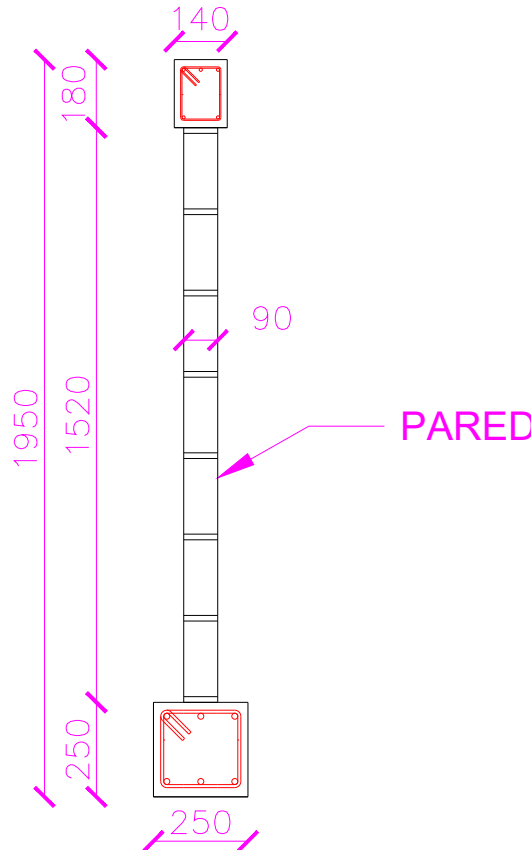


DOBLADO DE ESTRIBOS

Ø	dh	Ld
5.5	22	75
8	32	75

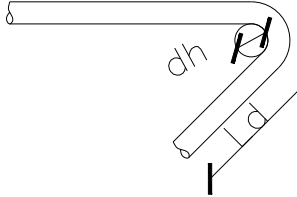

DOBLADO DE VARILLAS

Ø	dh
8	50
10	60
12	75
14	85
16	100
18	110
20	120
22	135
25	150
28	225
32	260

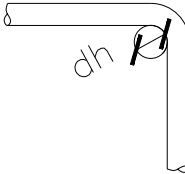

Volumen de Hormigón						
	b (mm)	h (mm)	L (mm)	Volumen (m³)	No.	Total (m³)
Zapata	700	250	700	0.1225	2	0.2450
Viga inferior	250	250	1300	0.0813	1	0.0813
Viga superior	140	175	2090	0.0512	1	0.0512
Columnas	172	172	1695	0.0501	2	0.1003
						0.4777

N° de Bloques Por definir

Acero de refuerzo												
	Diámetro (mm)	Área (mm²)	Longitud						Peso nominal (kg/m)	No.	Peso total (kg)	Observaciones
			a (mm)	b (mm)	c (mm)	d (mm)	e (mm)	Total (mm)				
Zapata	12	113	80	670	80	0	0	830	0.89	20	14.74	Refuerzo longitudinal
Viga inferior	16	201	190	2670	190	0	0	3050	1.58	6	28.88	Refuerzo longitudinal
	8	50	200	200	200	200	150	950	0.39	13	4.87	Estribos
Viga superior	8	50	100	2375	100	0	0	2575	0.39	2	2.03	Refuerzo longitudinal
	10	79	150	2395	150	0	0	2695	0.62	2	3.32	Refuerzo longitudinal
	4	13	110	145	110	145	60	570	0.10	52	2.92	Estribos
Columnas	12	113	150	1877	150	0	0	2177	0.89	4	7.73	Refuerzo longitudinal
	5.5	24	142	142	142	142	60	628	0.19	53	6.21	Estribos
											70.71	

NOV/2021	1	Entrega
FECHA	No.	DESCRIPCIÓN
REVISIONES		
OBRA:		
PRUEBAS		
CONTIENE:		
MURO 1		
DISEÑO ESTRUCTURAL: Ing. JOSÉ A. BARROS CABEZAS		RESPONSABILIDAD TÉCNICA:
REG. PROF. SENESCYT 1028-09-924698 Cel.: 0993-265998 - jo_cbarros@hotmail.com		
Obra No.: 0021	Fecha: NOV/2021	Escala: Se indican No.: 1/4